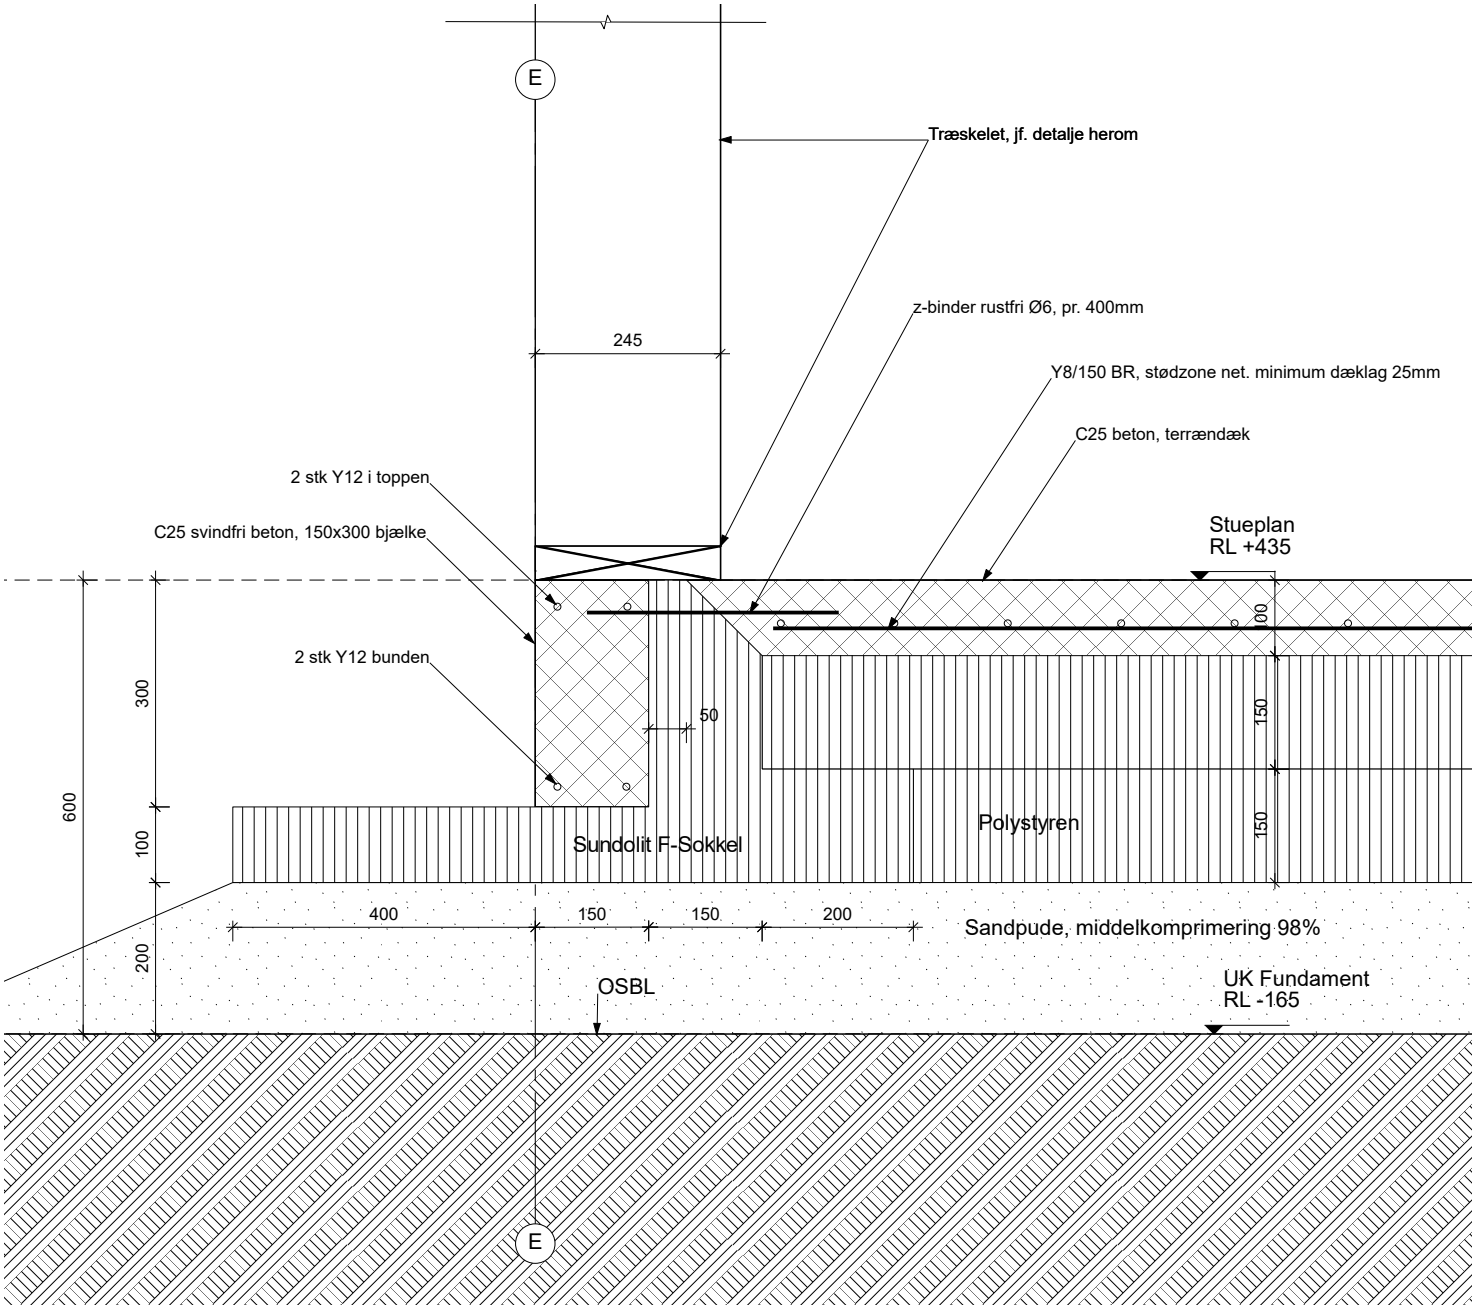

1 Fundaments detalje
1:10

SIGNATUR
- Skraveringer mm. angives minimum en gang på tegninger

HENVISNINGER
- De vist snit, detaljer og henvisninger samt afledte henvisninger heraf udgør den samlede tegning.

NOTE GENERELT
- Alle mål skal altid kontrolleres op mod faktiske forhold, tegninger er ikke produktionstegninger
- Afviger forhold stoppes arbejdet og rådgiver kontaktes
- For specifikationer mm. henvises til generel noten.
- Producent-, SBI-, Bygerfa-anvisninger samt BR18 følges.
- Nærværende er konstruktionstegninger og dækker ikke over byggeriet generelle byggeteknik.
- Arkitekt model danner grundlag for geometrien på tegninger.
- Målestok er anvist på de individuelle elementer/views. Nordpil gælder kun for plantegninger

V11_K09_H5_EX_S1_1-_Fundaments detalje

-	-	-	-	-	-
		-	-	-	-
Rev.:	***Dato:***	***Tegn.:***	***KS.:***	***Godk.:***	***Beskrivelse:***
	03.10.2024	DBO	DBO	DBO	Udgivet

Sags nr. - navn - adresse: 240054 - Nybyg Nybovej 11 - Nybovej 11 7400 Herning

Bygherre - adresse: Anne-louise og Mikkel Asmussen - Odinsgade 6 1. 7400 Herning

Projekt ID:	VA11	***Fag:***	K09, Konstruktion
Filtype:	F1, tegningsfil	***Tegn.type:***	H5 - detalje
Etage:	EX - flere etager	***Stade:***	S1, Fremtidige forhold
Tegningsnr.:	V11_K09_H5_EX_S1_1	***Emne:***	Fundaments detalje
Fase:	Hovedprojekt	***Format:***	A4

OCplan ApS
Odinsgade 6, 7400 Herning
Cvr nr.: 42665797
info@ocplan.dk
www.ocplan.dk

OCplan beregnet til at bygge