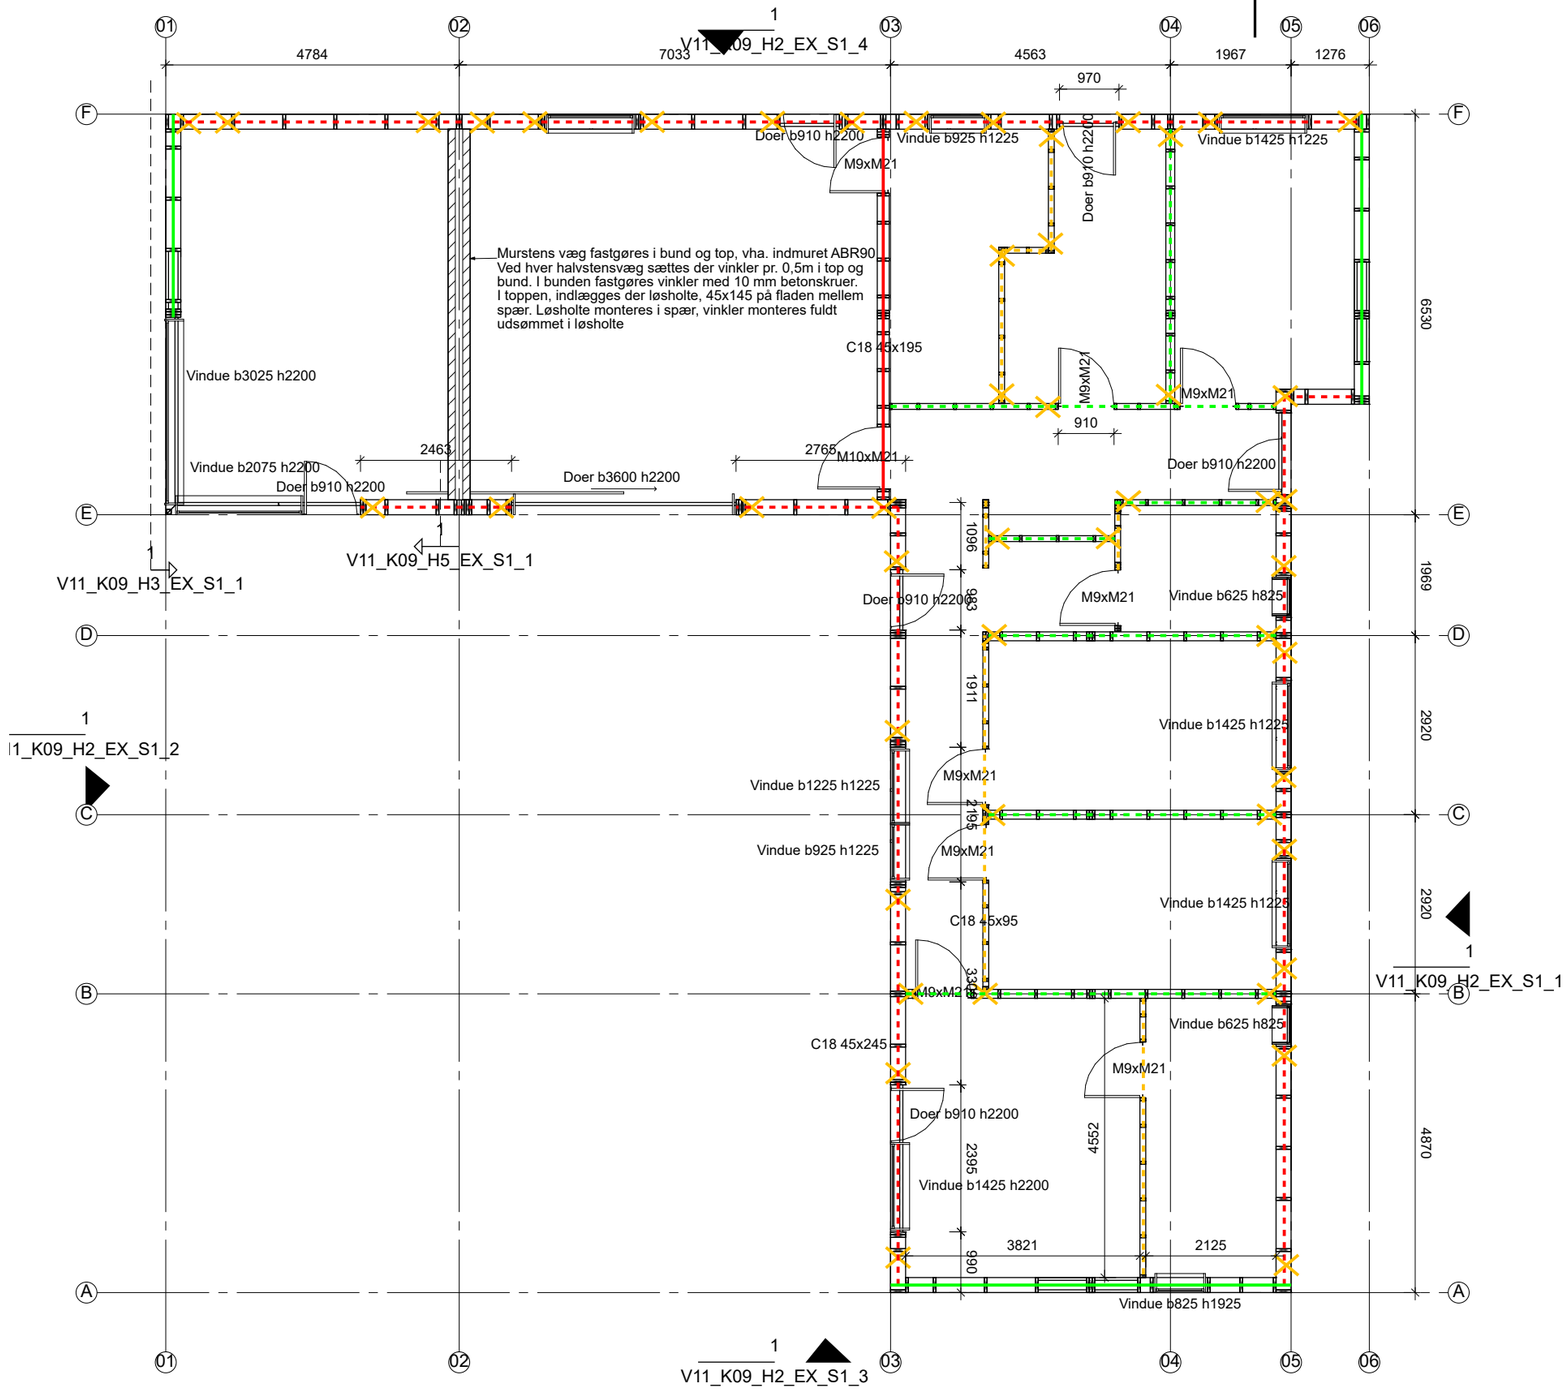

1 Stueplan fastgørelse vægge b
1:100

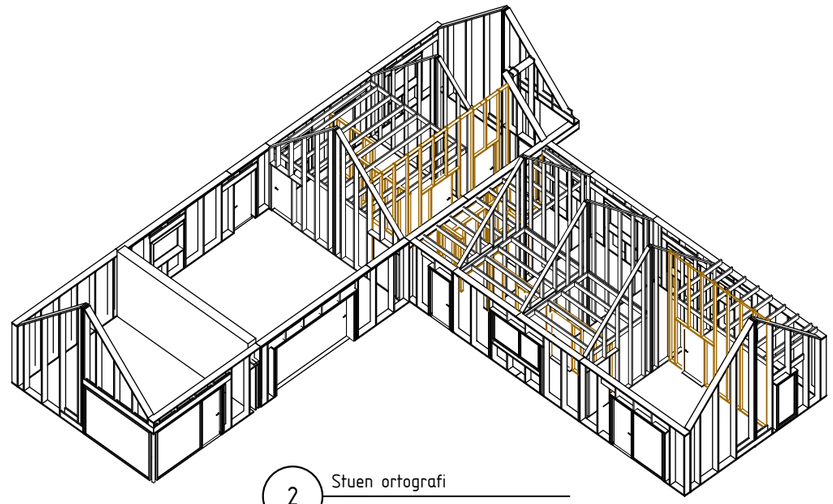

2 Stuen ortografi
1:200

NORTH

Fastgørelser bunden af vægge

Fuldt optrukket linjer fastgøres med M10 klæbeanker, sættedybe 100mm
Klæb, Hilti HIT-HY 170, gevind stand minimum 5.8 stål
Stiplet linjer fastgøres med SPIT TAPCON HFL 6/100/65-45

- M10 klæbe anker, 1 stk. pr m.
- M10 klæbe anker, 1 stk. pr 0,75m.
- M10 klæbe anker, 1 stk.
- TAPCON HFL, 2 stk. pr m.
- TAPCON HFL, 1 stk. pr m.
- TAPCON HFL, 0,5 stk. pr m.

SIGNATUR
- Skraveringer mm. angives minimum en gang på tegninger

HENVISNINGER
- De vist snit, detaljer og henvisninger samt afledte henvisninger heraf udgør den samlede tegning.

NOTE GENERELT
- Alle mål skal altid kontrolleres op mod faktiske forhold, tegninger er ikke produktionstegninger
- Afviger forhold stoppes arbejdet og rådgiver kontaktes
- For specifikationer mm. henvises til generel noten.
- Producent-, SBI-, Bygerfa-anvisninger samt BR18 følges.
- Nærværende er konstruktionstegninger og dækker ikke over byggeriet generelle byggeteknik.
- Arkitekt model danner grundlag for geometrien på tegninger.
- Målestok er anvist på de individuelle elementer/views. Nordpil gælder kun for plantegninger

V11_K09_H1_ES_S1_2-None_Stueplan fastgørelser vægge bund

Rev.:	Dato:	Tegn.:	KS.:	Godk.:	Beskrivelse:
-	-	-	-	-	-
A	-	-	-	-	-
None	15.09.2024	DBO	DBO	DBO	Udgivet

Sags nr. - navn - adresse: 240054 - Nybyg Nybovej 11 - Nybovej 11, 7400 Herning

Bygherre - adresse: Annelouise og Mikkel Asmussen - Odinsgade 6, 1., 7400 Herning

Projekt ID:	VA11	**Fag:**	K09, Konstruktion
Filtype:	F1, tegningsfil	**Tegn.type:**	H1, plan
Etage:	ES, Stuen	**Stade:**	S1, Fremtidige forhold
Tegningsnr.:	V11_K09_H1_ES_S1_2	**Emne:**	Stueplan fastgørelser vægge bund
Fase:	Hovedprojekt	**Format:**	A3

OCplan ApS
Odinsgade 6, 7400 Herning
Cvr nr.: 42665797
info@ocplan.dk
www.ocplan.dk

OCplan beregnet til at bygge